


SPECIFIC PURPOSE SURVEY
PROJECT LOCATION

NOTICE: UNDERGROUND AND
SUBAQUEOUS IMPROVEMENTS
WERE NOT LOCATED AS PART
OF THIS SURVEY

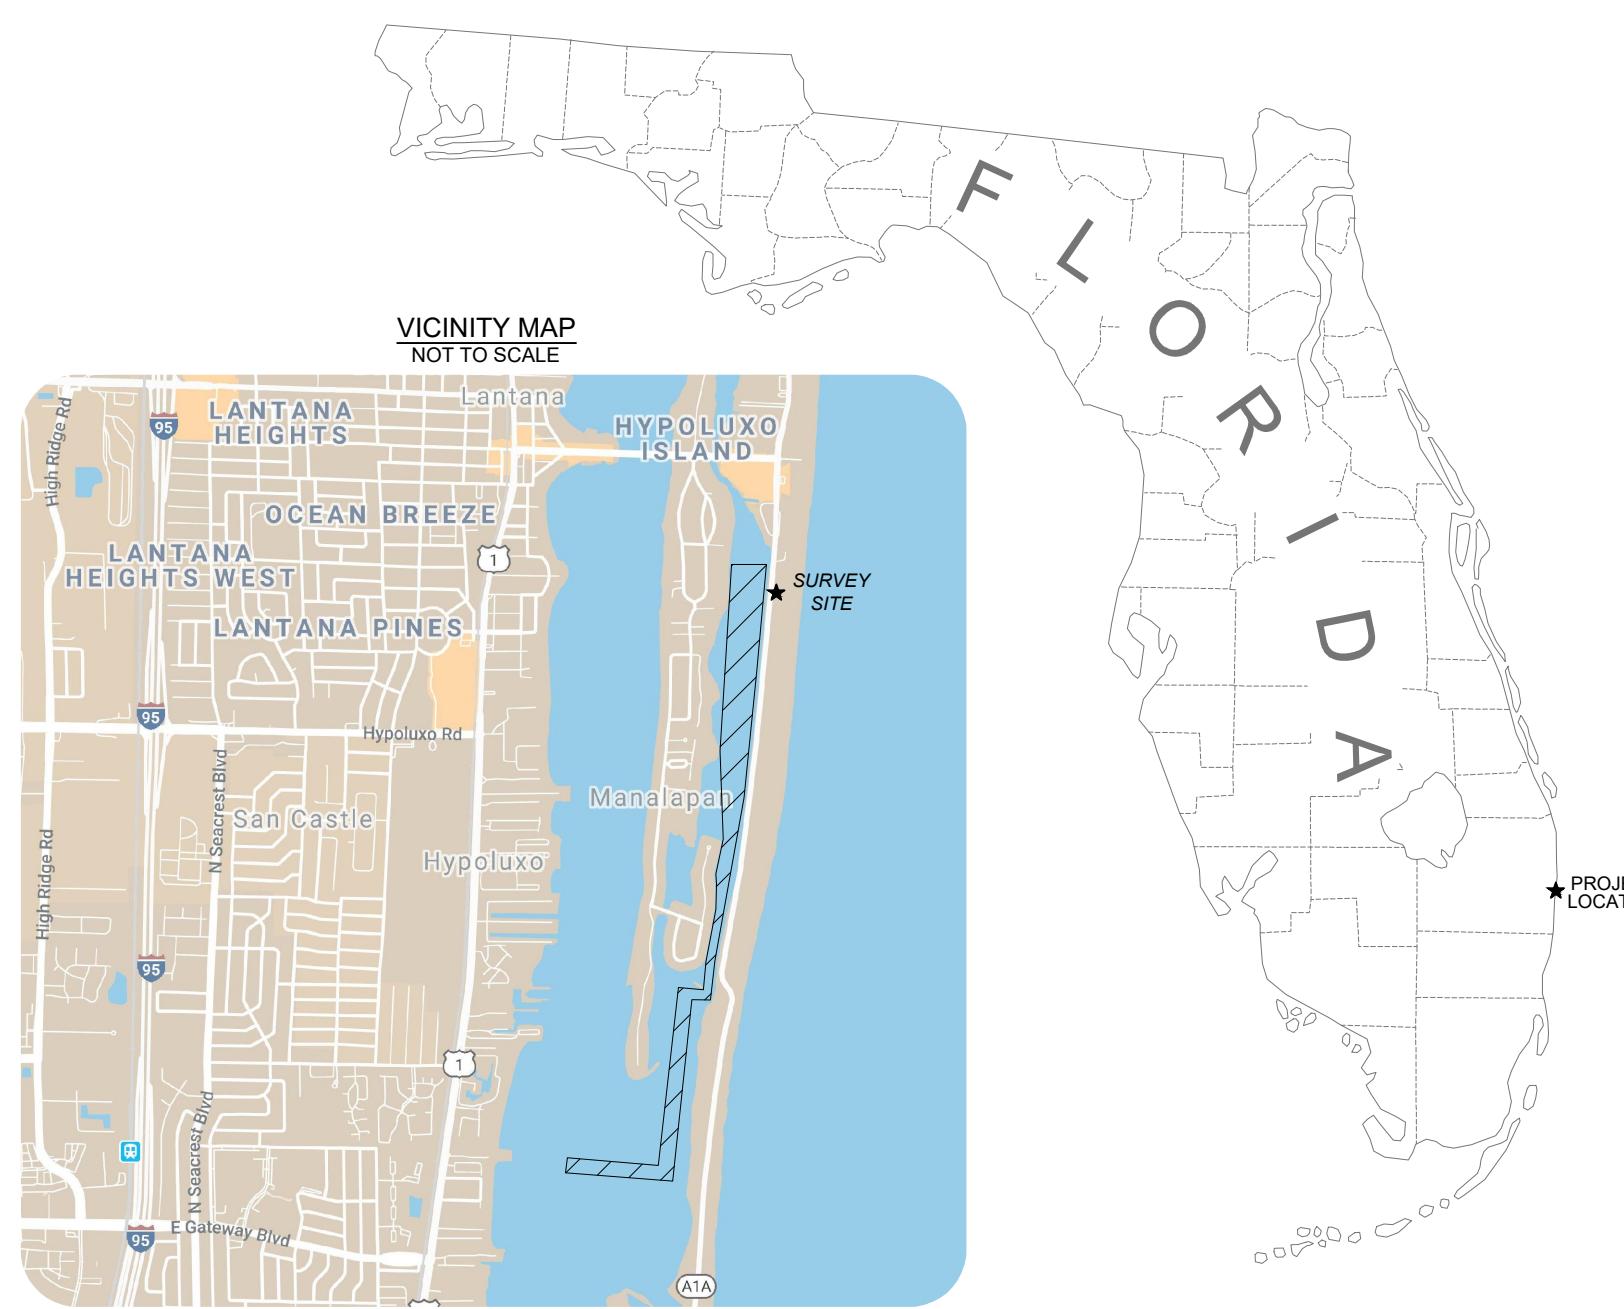


SURVEY NOTES:

1. THIS IS NOT A BOUNDARY SURVEY. THIS IS A SPECIFIC PURPOSE SURVEY AS DEFINED IN THE STANDARDS OF PRACTICE FOR SURVEYING AND MAPPING IN CHAPTER 5J-17 FLORIDA ADMINISTRATIVE CODE.
2. THIS SURVEY IS CERTIFIED TO ANTHONY & BONNIE ROBBINS AND THE CHAPPELL GROUP, INC.
3. THIS SURVEY IS PROVIDED EXCLUSIVELY FOR THE USE THOSE TO WHOM IT IS CERTIFIED. IT IS NOT TO BE USED BY OTHERS FOR CONSTRUCTION, PERMITTING, DESIGN OR ANY OTHER USE WITHOUT THE WRITTEN CONSENT OF TERRAQUATIC, INC.
4. THIS SURVEY, AND ANY REPRODUCTION THEREOF, IS NOT VALID WITHOUT AN ORIGINAL OR VERIFIED DIGITAL SIGNATURE AND SEAL OF A FLORIDA REGISTERED SURVEYOR. ADDITIONALLY, THIS SURVEY IS NOT VALID IF PRINTED BEARING A DIGITAL SIGNATURE AND SEAL.
5. OTHER THAN AS SHOWN ON THE SURVEY, A SEARCH OF THE PUBLIC RECORDS WAS PERFORMED FOR ENCUMBRANCES, ENCUMBRANCES OR OTHER INSTRUMENTS OF RECORD WHICH MAY AFFECT THIS PARCEL OF LAND.
6. THIS MAP IS INTENDED TO BE DISPLAYED AT A SCALE OF 1" = 300' (COVER) AND 100' (CONTOUR MAP) OR SMALLER.
7. UNDERGROUND UTILITIES WERE NOT LOCATED AS PART OF THIS SURVEY.
8. GEOGRAPHIC AND PLANE COORDINATES SHOWN HERON ARE RELATIVE TO THE NORTH AMERICA DATUM OF 1983, FLORIDA STATE PLANE, ZONE 901, TRANSVERSE MERCATOR PROJECTION IN THE U.S. SURVEY FOOT UNIT OF MEASUREMENT.
9. LOCATIONS OF ALL IMPROVEMENTS WERE OBTAINED USING REAL TIME KINEMATIC GPS METHODOLOGIES WITH BROADCAST CORRECTIONS FROM THE FLORIDA DEPARTMENT OF TRANSPORTATION REFERENCE NETWORK. COORDINATES ARE IN FEET.
10. THE SPECIFIC PURPOSE OF THIS SURVEY IS TO SHOW THE GENERAL SEAFLOOR CONDITIONS OF A PORTION OF THE LAKE WORTH LAGOON IN LANTANA AND MANALAPAN, FL.
11. HYDROGRAPHIC (BATHYMETRIC) DATA WERE COLLECTED UTILIZING AN ODOM CV100 SURVEY GRADE SOUNDER WITH A 200KHZ TRANSDUCER IN CONJUNCTION WITH REAL TIME KINEMATIC GPS METHODOLOGIES WITH BROADCAST CORRECTIONS FROM THE FLORIDA DEPARTMENT OF TRANSPORTATION REFERENCE NETWORK. DEPTHS ARE ACCURATE TO +/- 0.5 FT.
12. CONTOURS WERE COMPUTER GENERATED AND INTERPOLATED FROM SURVEY TRANSECTS SPACED AT FIFTY FOOT (50') INTERVALS AND CAN ONLY BE CONSIDERED AS INDICATING THE GENERAL SEAFLOOR CONDITIONS EXISTING AT THE TIME OF THE SURVEY.

LEGEND:

APX	APPROXIMATE
PSM	PROFESSIONAL SURVEYOR
MLW	MEAN LOW WATER
NAVD-88	NORTH AMERICAN VERTICAL DATUM OF 1988
TYP	TYPICAL

HYDROGRAPHIC DATA ARE RELATIVE TO MEAN
LOW WATER AND REFERENCED TO FLORIDA
DEPARTMENT OF ENVIRONMENTAL
PROTECTION TIDE STATION NUMBER 872-2706.
LOCAL VERTICAL DATUM DIAGRAM
TIDAL EPOCH: 1983 - 2001
NAVD-88
MLW -2.16'
MLLW -2.30'
CONTOURS ARE AT 1' INTERVALS.

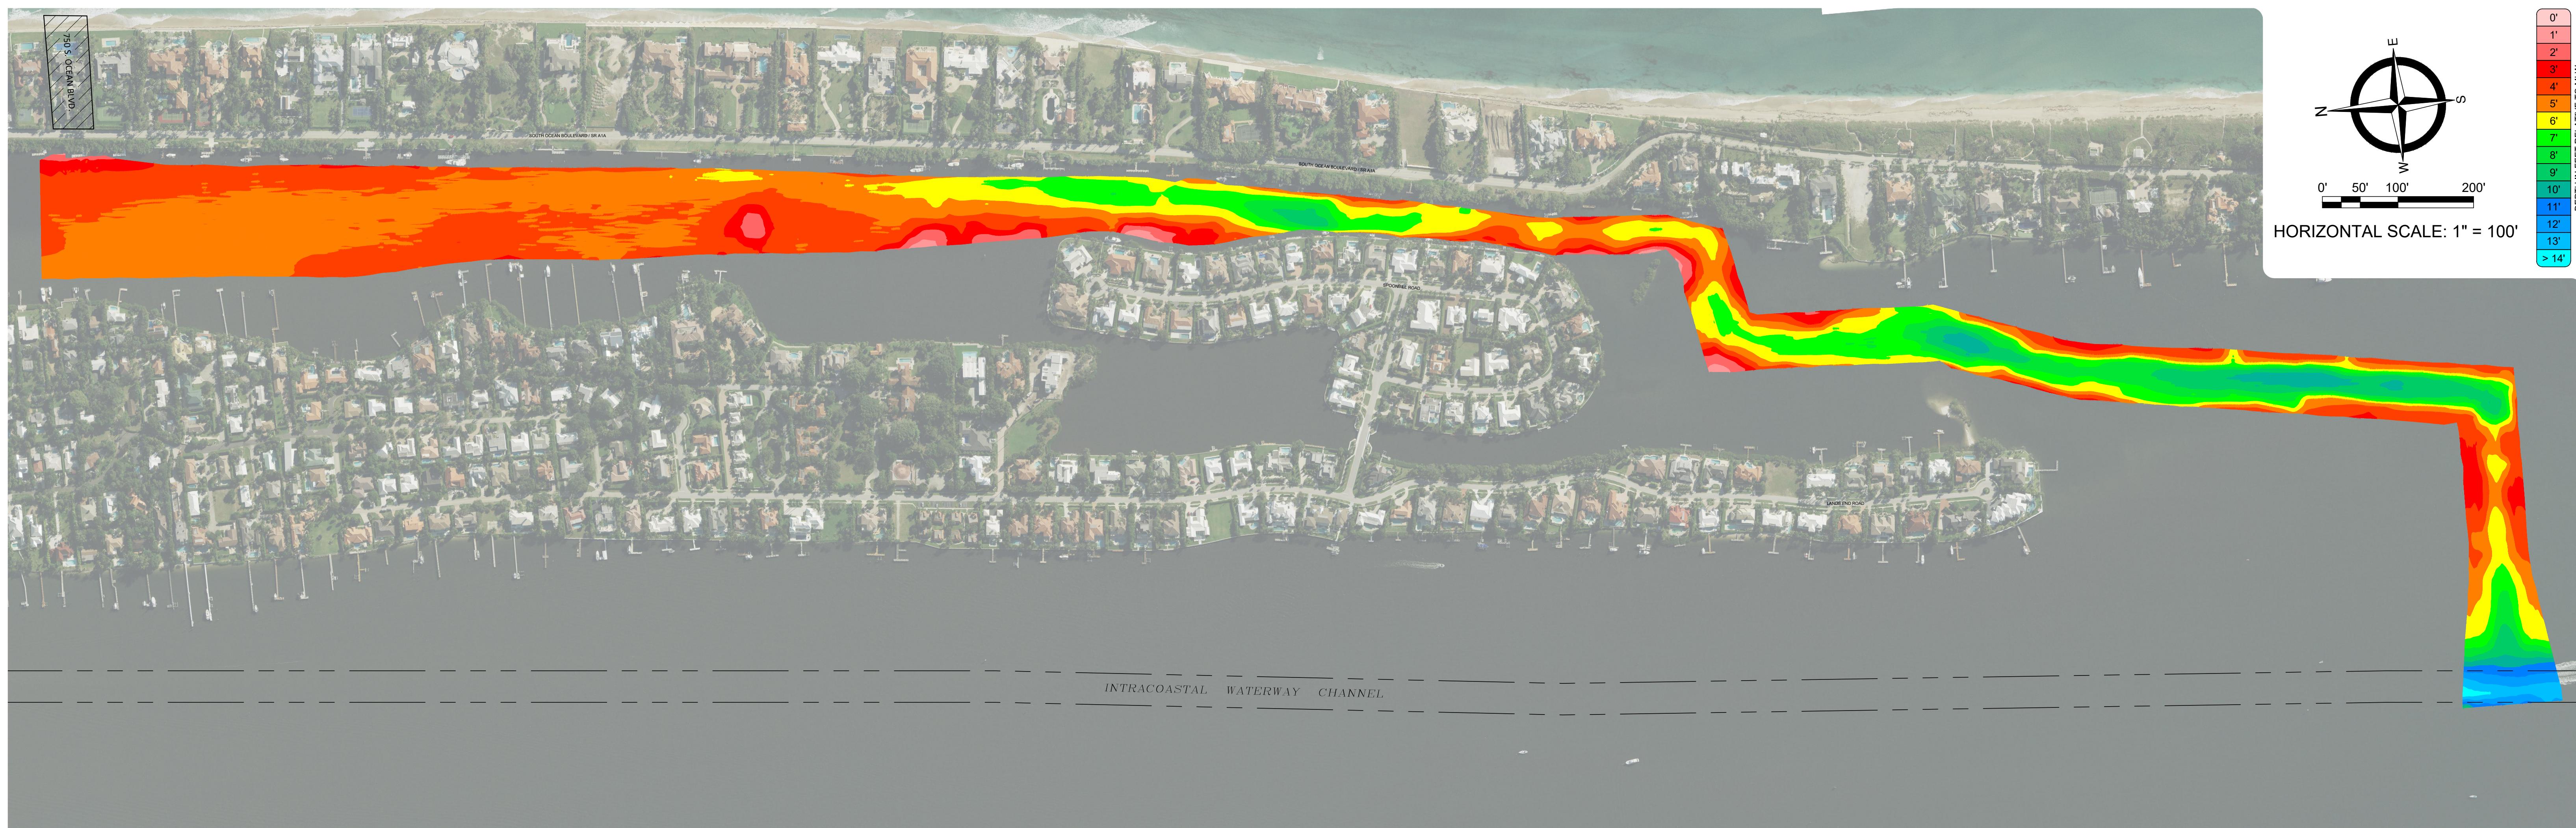

PREPARED FOR:



714 EAST McNAB ROAD
POMPANO BEACH, FLORIDA 33060



TERRAQUATIC, INC. - PHONE: (561) 400-8348
1220 TANGELO TERR, UNIT A12 - DELRAY BEACH, FLORIDA 33444


CERTIFICATION:

KENNETH C. JACKSON, PSM
FLORIDA REGISTRATION LS4549 - CERTIFICATE OF AUTHORIZATION NO. 7324

750 S. OCEAN BLVD.
HYDROGRAPHIC SURVEY
COVER SHEET
MANALAPAN - PALM BEACH COUNTY, FLORIDA

DRAWN BY: BL	CHECKED BY: KCJ	SHEET
JOB No.: 20-943	DATE: 2/20/20	
REV	DESCRIPTION	DATE

1
of 3

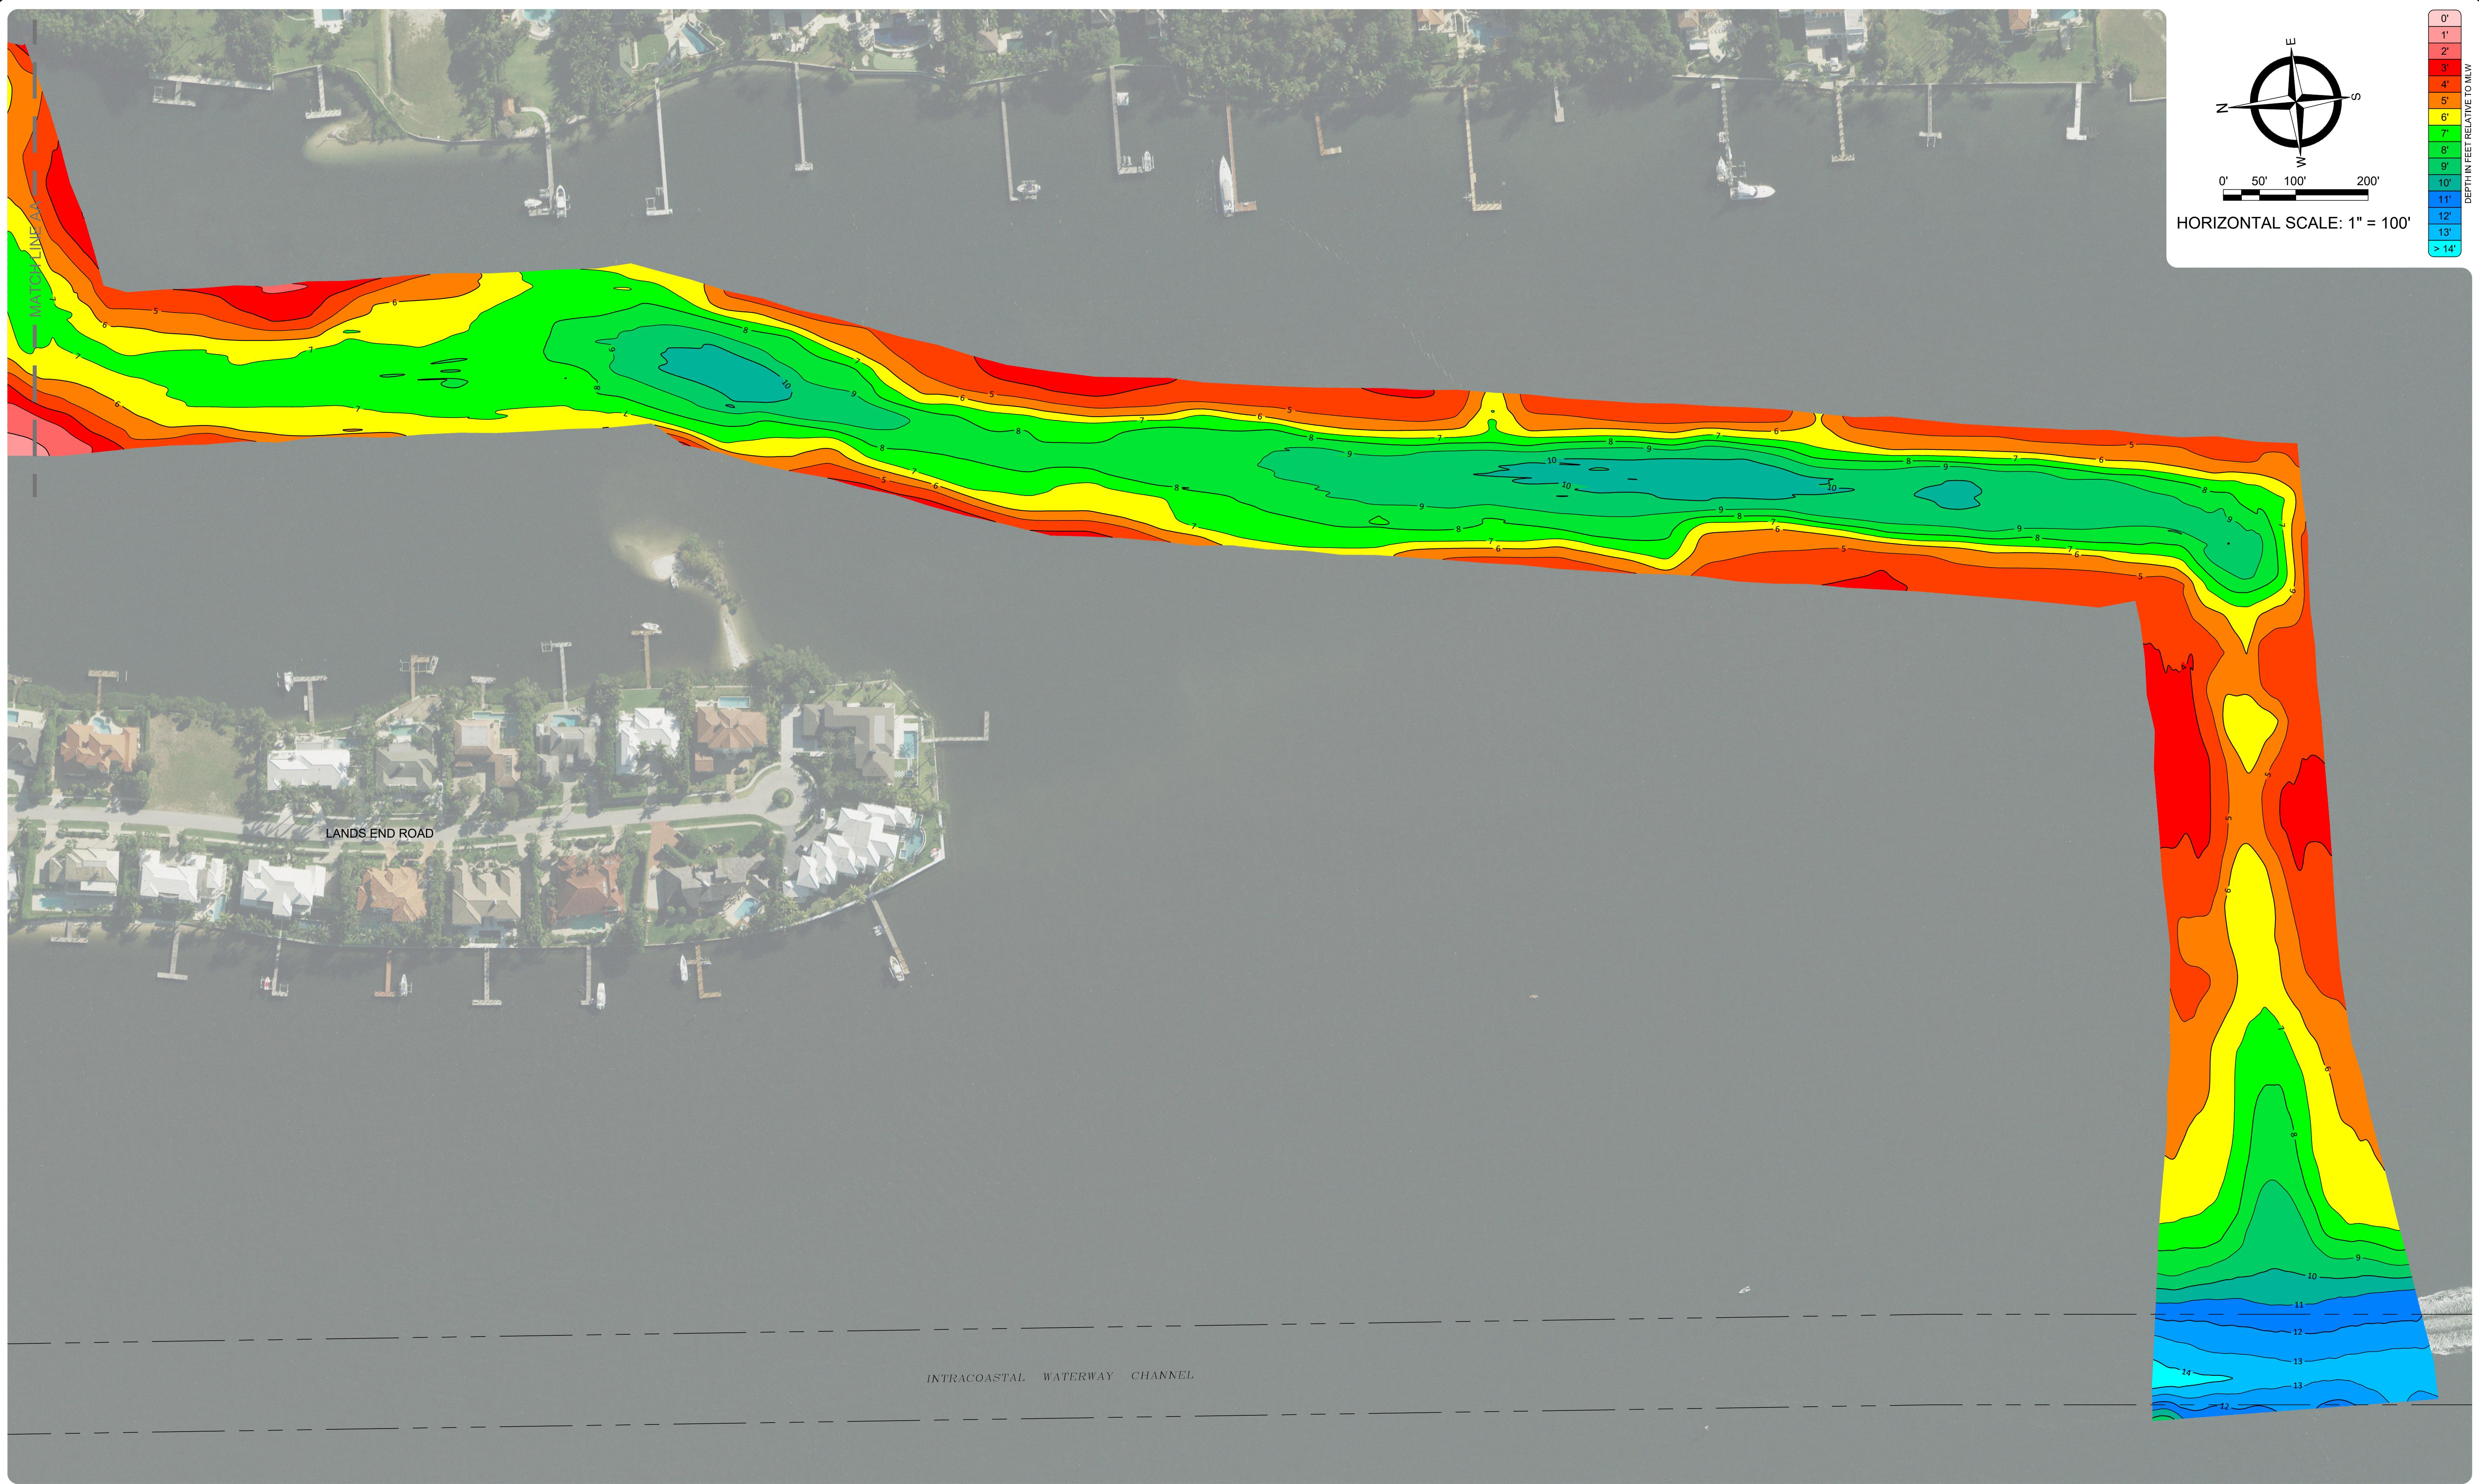

PREPARED FOR:



714 EAST McNAB ROAD
POMPANO BEACH, FLORIDA 33060


TERRAQUATIC
SURVEYING AND MAPPING

TERRAQUATIC, INC. - PHONE: (561) 400-8348
1220 TANGELO TERR, UNIT A12 - DELRAY BEACH, FLORIDA 33444

750 S. OCEAN BLVD.
HYDROGRAPHIC SURVEY
CONTOUR MAP
MANALAPAN - PALM BEACH COUNTY, FLORIDA

DRAWN BY: BL	CHECKED BY: KCJ
JOB No.: 20-943	DATE: 2/20/20
REV	DESCRIPTION

SHEET
2
of 3

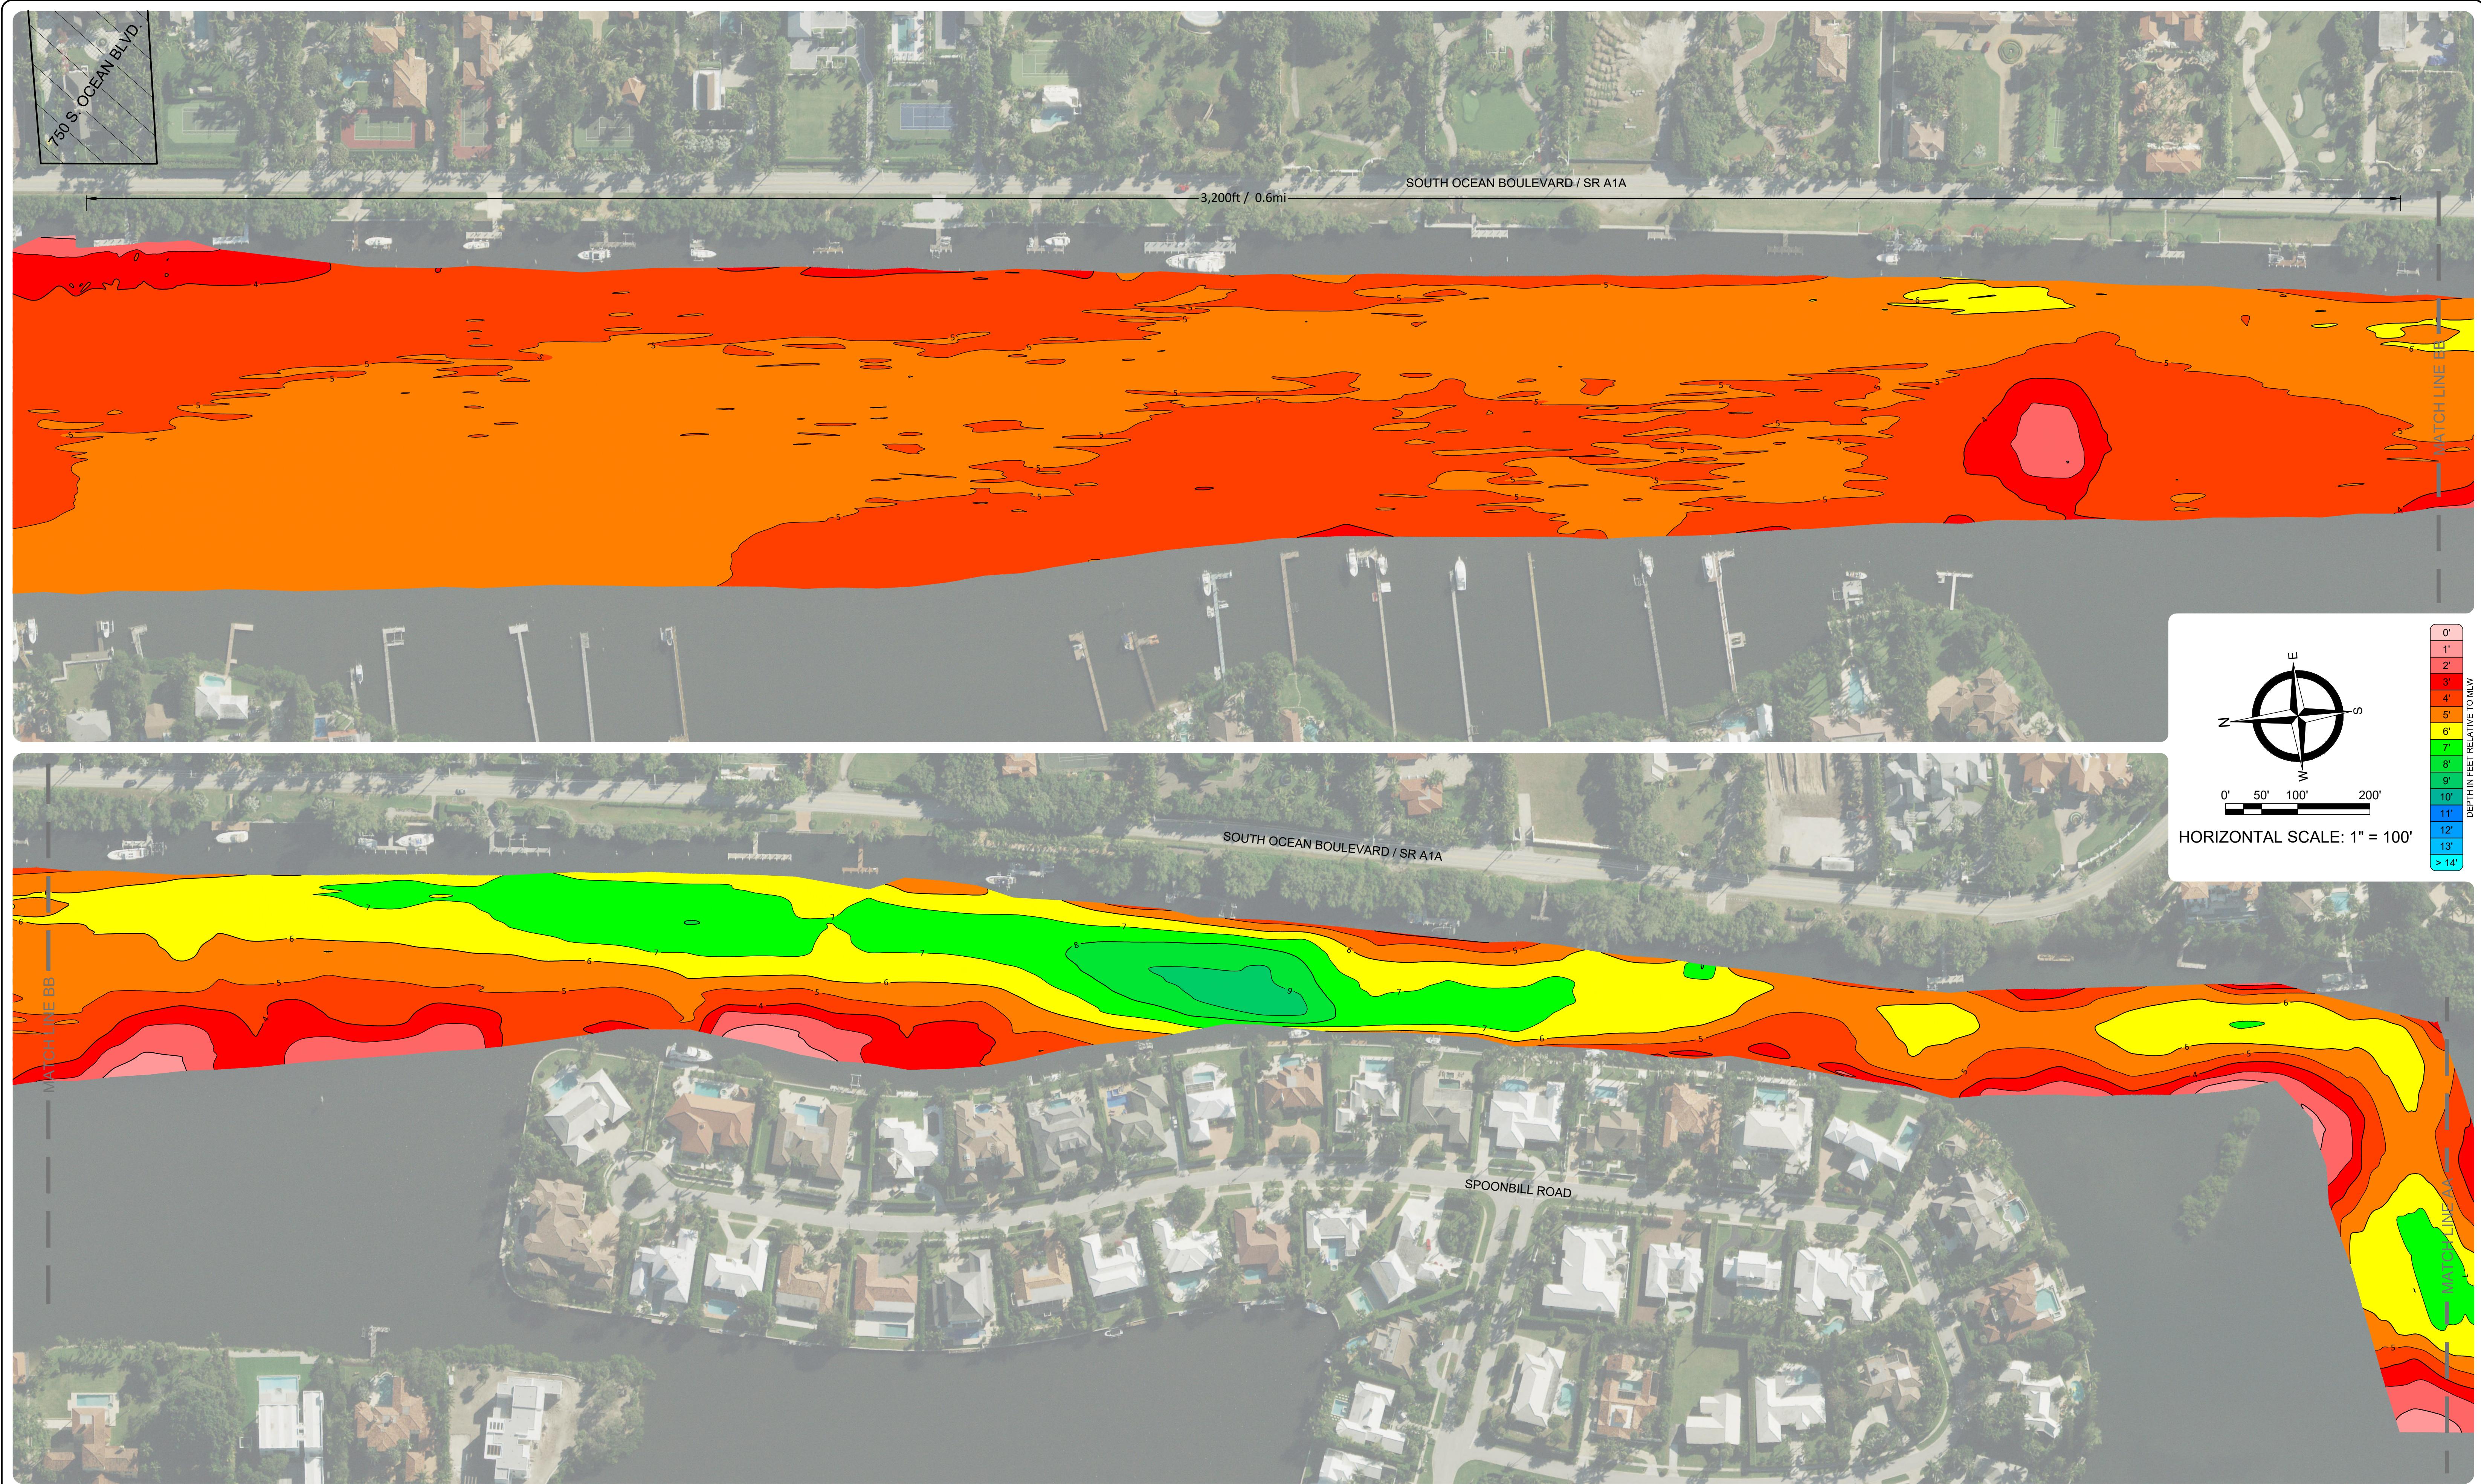

PREPARED FOR:



**714 EAST McNAB ROAD
POMPANO BEACH, FLORIDA 33060**

The logo for TERRAQUATIC SURVEYING AND MAPPING. The word "TERRAQUATIC" is written in large, bold, black capital letters. A blue wavy line starts from the top of the letter "T" and flows down through the letters "R", "A", "U", "A", "T", and "I", ending at the bottom of the letter "C". Below "TERRAQUATIC" in smaller black capital letters is the text "SURVEYING AND MAPPING".

TERRAQUATIC, INC. - PHONE: (561) 400-8348

1220 TANGELO TERR, UNIT A12 - DELRAY BEACH, FLORIDA 33444

750 S. OCEAN BLVD.
HYDROGRAPHIC SURVEY
CONTOUR MAP
ANALAPAN - PALM BEACH COUNTY, FLORIDA

SHEET 3 of 3